


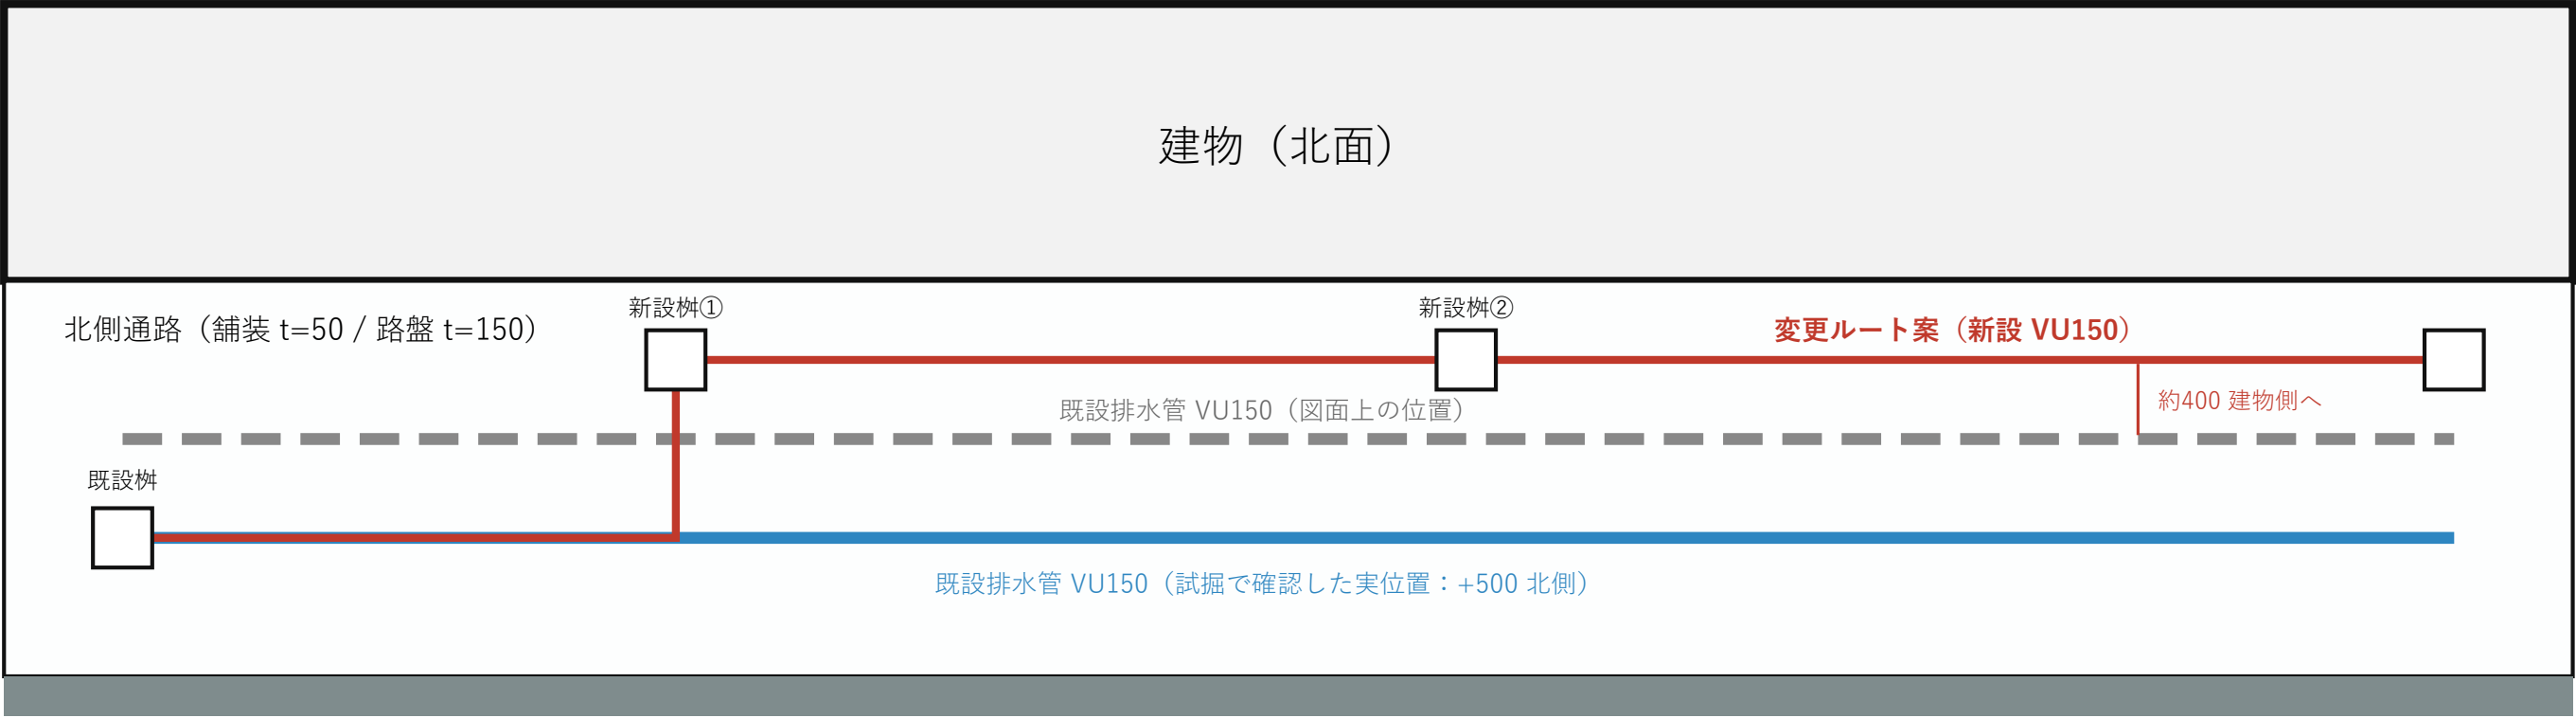

仮囲い（移設予定）

特記

- ・ 11/9 試掘にて既設排水管が設計図より約500mm北側にあることを確認
- ・ 新設排水管は建物側（南側）へ約400mm振り、既設管との離隔を確保する（森田設計 11/10 回答）
- ・ 勾配 1/100 以上確保のこと（既設枳への接続高さは変更なし）



工事名	（仮称）港南三丁目オフィスビル新築工事		
図面名	外構 北側通路 排水ルート図		
図番	G-021 (Rev.1)	縮尺	1/100
作成	東都建設 港南三丁目作業所	日付	2026.11.10