



① 配置図（地上：搬入車両ルート・クレーン位置）

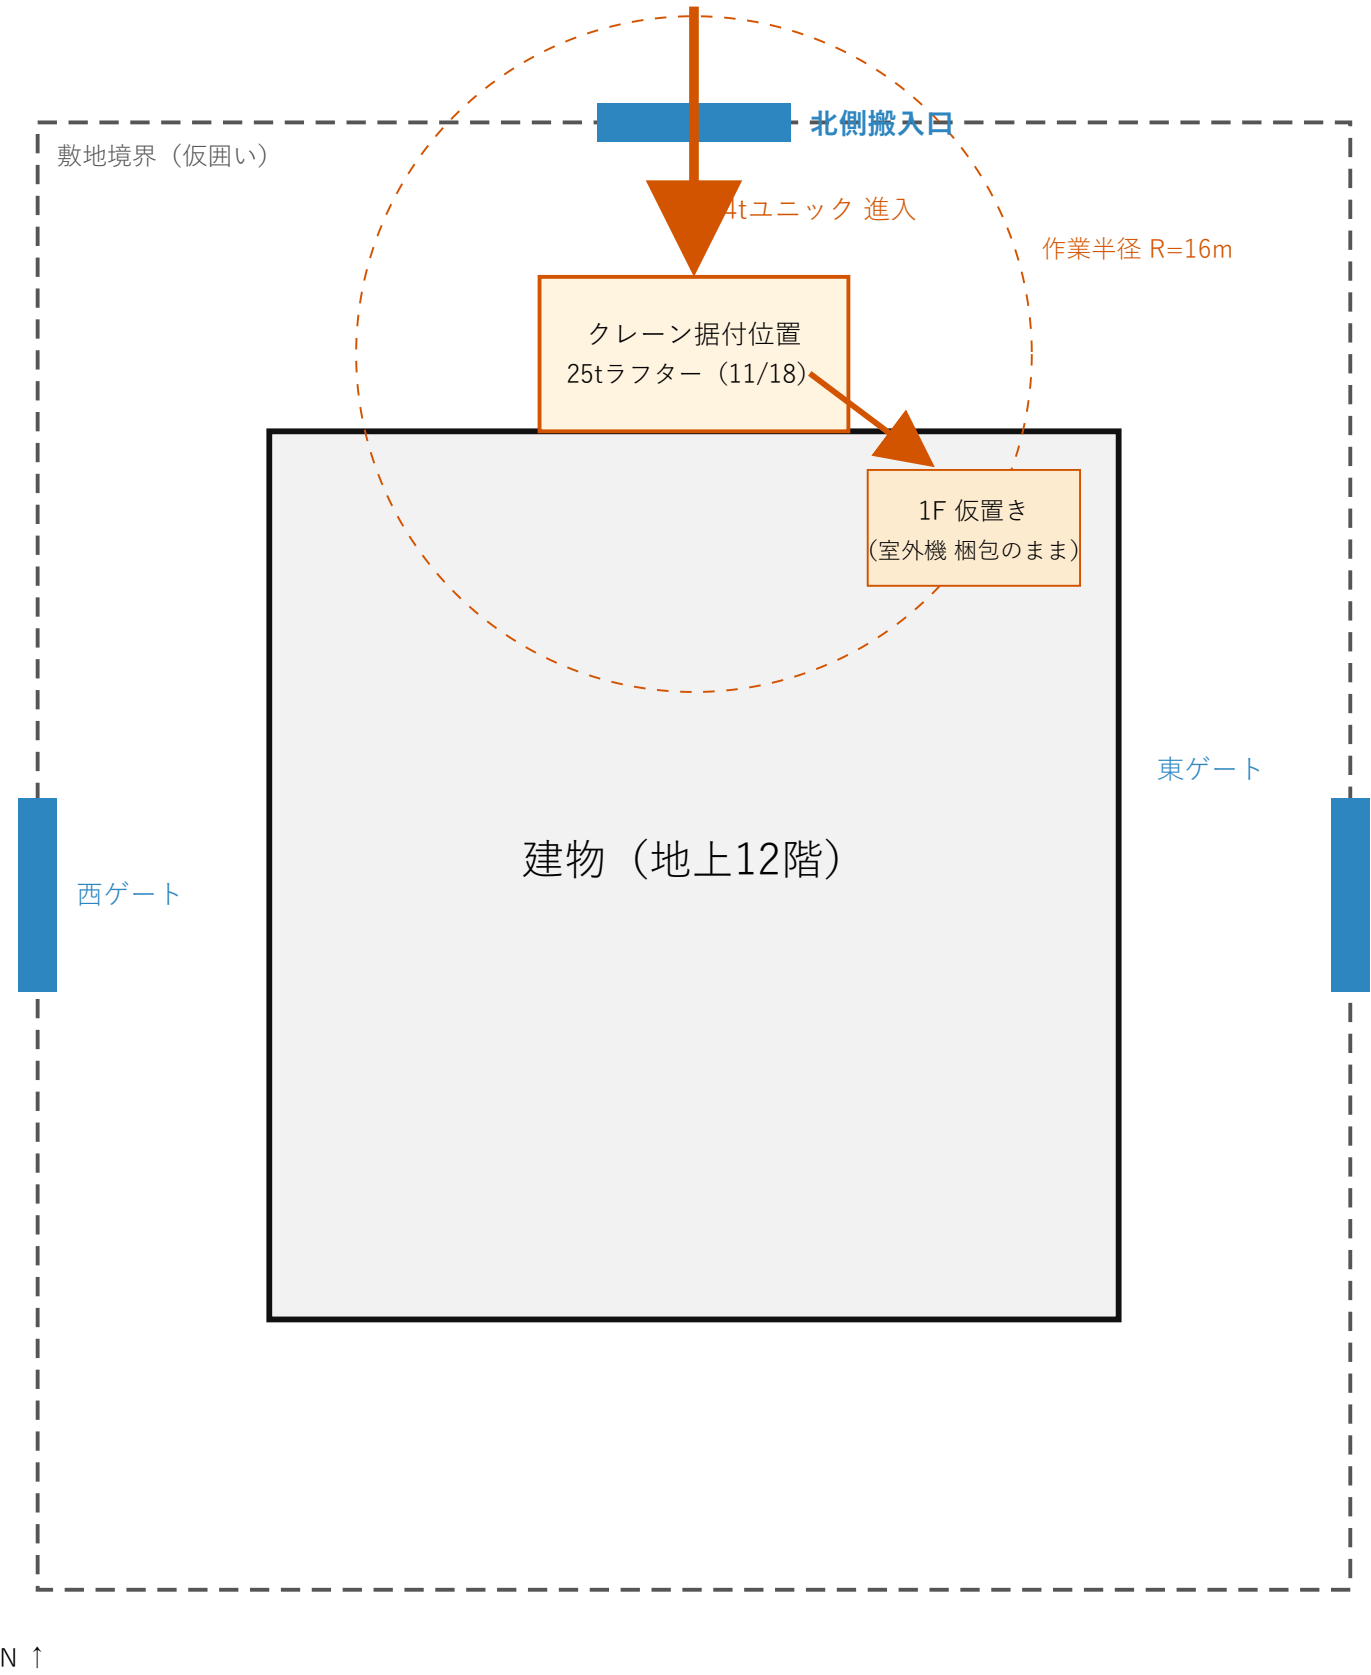

② 屋上伏図（荷取り・据付位置）

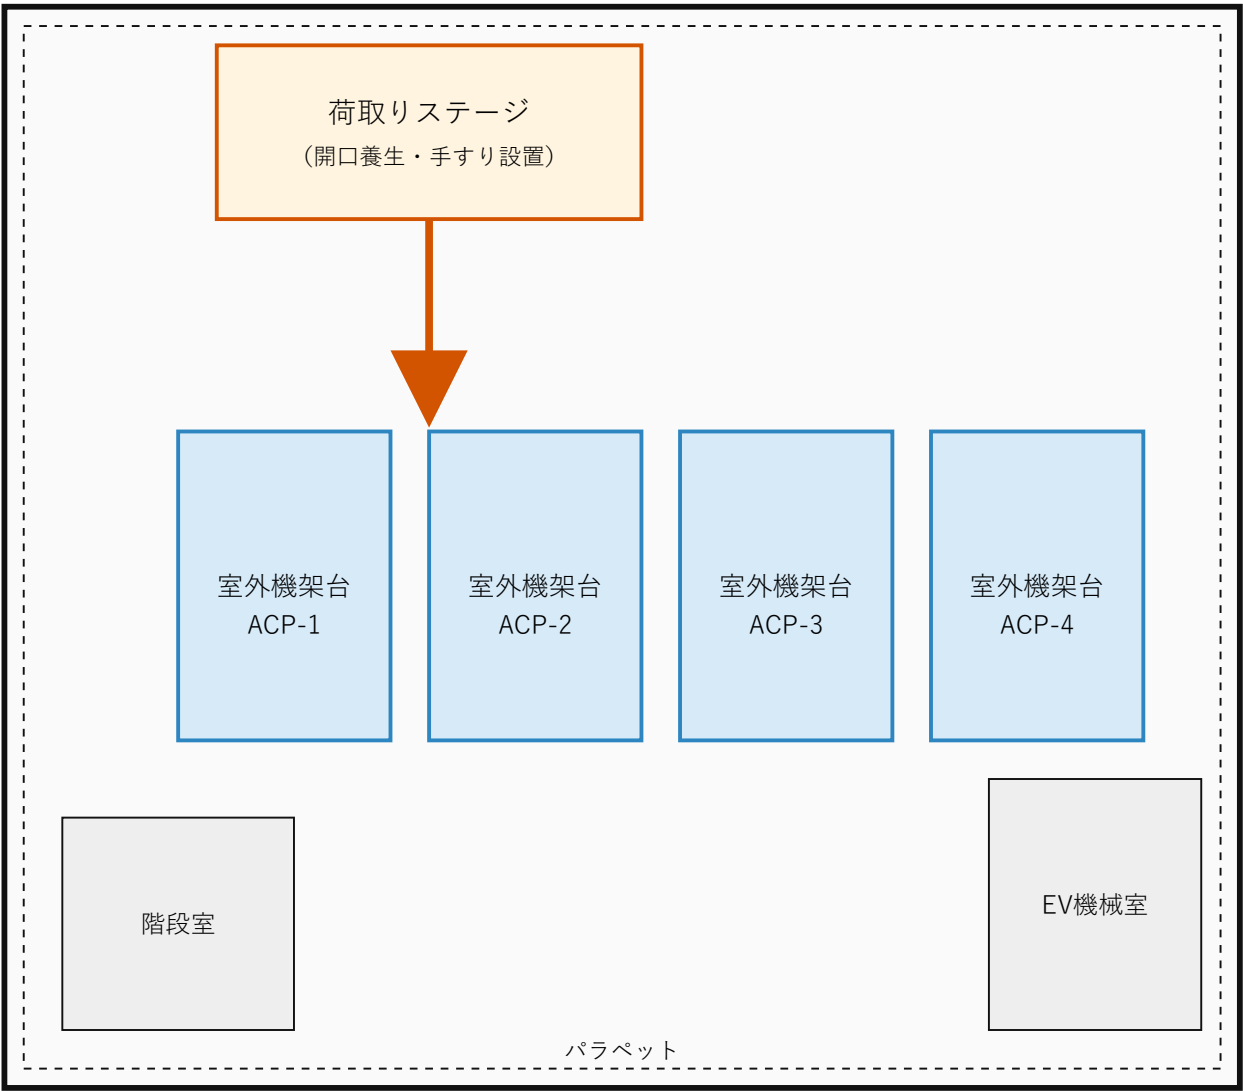

【搬入手順】

1. 11/12 8:30 4tユニック2台で北側搬入口より搬入、1F仮置き（シート養生）
2. 11/18 25tラフターを北側に据付、荷取りステージへ揚重
3. 屋上はハンドリフト・チェンブロックで架台まで小運搬、据付
4. 吊荷の下は立入禁止（北側通路は揚重中 通行止め、誘導員2名）

※揚重計画書は富士空調システムより別途提出のこと

工事名	（仮称）港南三丁目オフィスビル新築工事		
図面名	屋上機器 搬入ルート図		
図番	KT-仮-031	縮尺	1/300（参考）
作成	東都建設 港南三丁目作業所	日付	2026.11.04